

שם פרויקט:

זוהר מור יודסך

כתובת:

שלונסקי 53 - דניה

א.ב. עיצובים

טל-0544211412 דקס-04-8744831
0528085083
etimealeve@gmail.com

- [illegible]

[illegible]

סד הדין:

סמך תוכנית:

בניה חדשה קרקע

קומרה:

17/09/2026

הדורה	אדרי אחראי
זמן גליון: A1	זמן הפקה
רשט: מרי	קרימ: 1:??
ליני ממן	

13

המבצע אחראי לבדיקת המידות ולהתאמתן במקום, על כל אי התאמה יש להודיע למתכננת ולהמתין לתשובה לפני המשך העבודה. ש לבצע איטום בכל החדרים הרטובים על פי התקן.

בניה קיימת

בניה חדשה קירות גבס

בניין זה שכן ברחוב

לבצע את כלל התוכניות
אישור קונסטרוקטור בלבד
המעצבת אחראית
שינויים מוצעים אלו.

ר ומהחלקה של קירות
ים, לפי תוכנית בניה זו
קה חדשה מקירות גבס
ל בידוד בצמר סלעים
יסות גבוהה

לתת חיזוקים נדרשים
רות לארון אמבטיה תלוי

בנייה של כל הקירות המסומנים כולל פתחים עבור דלתות

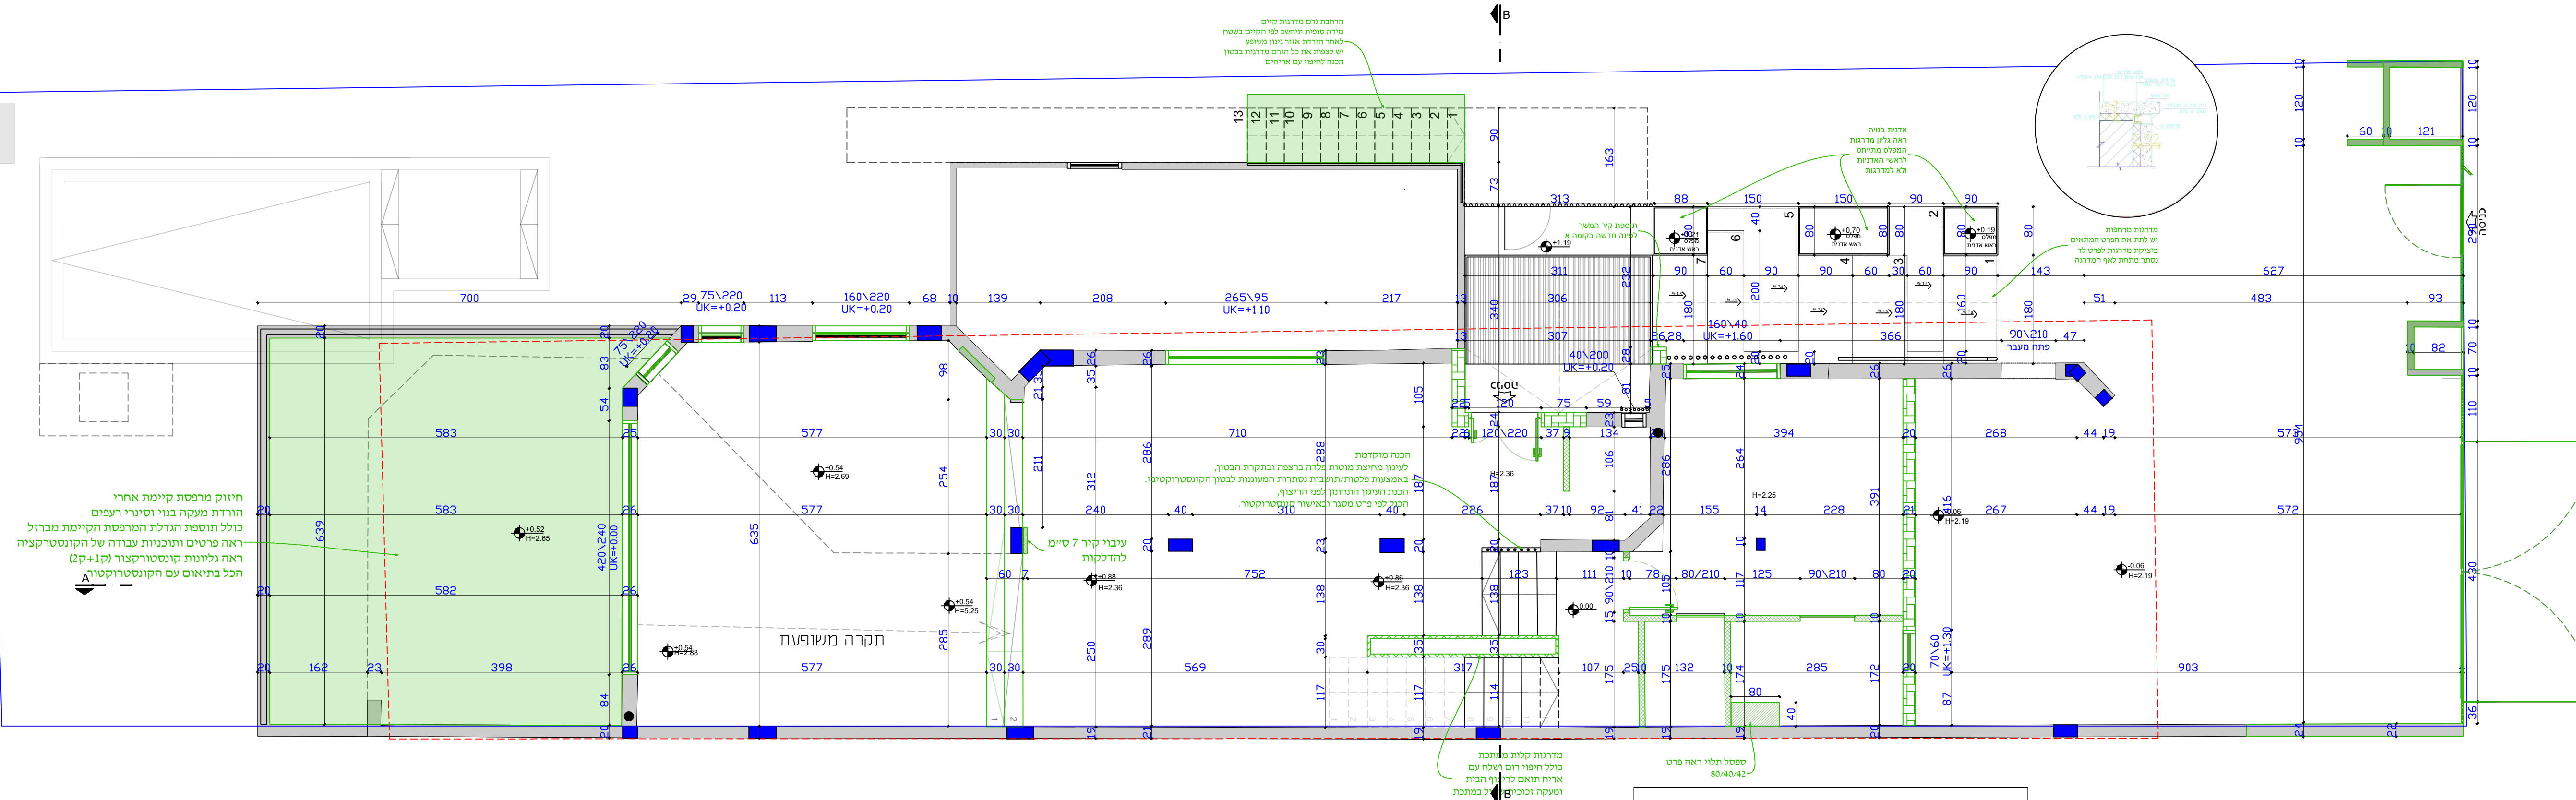
בנייה של חדרי הרחצה - קומפלט - ראה פריסות

החלפת כל הדלתות – קומפלט

הדבקת ריצוף

מסבא חדש - דאא תוכנית

ותיקון טיול וצביעה מחדש שם

[illegible]

חתך ספסל תלוי מיפואסי

